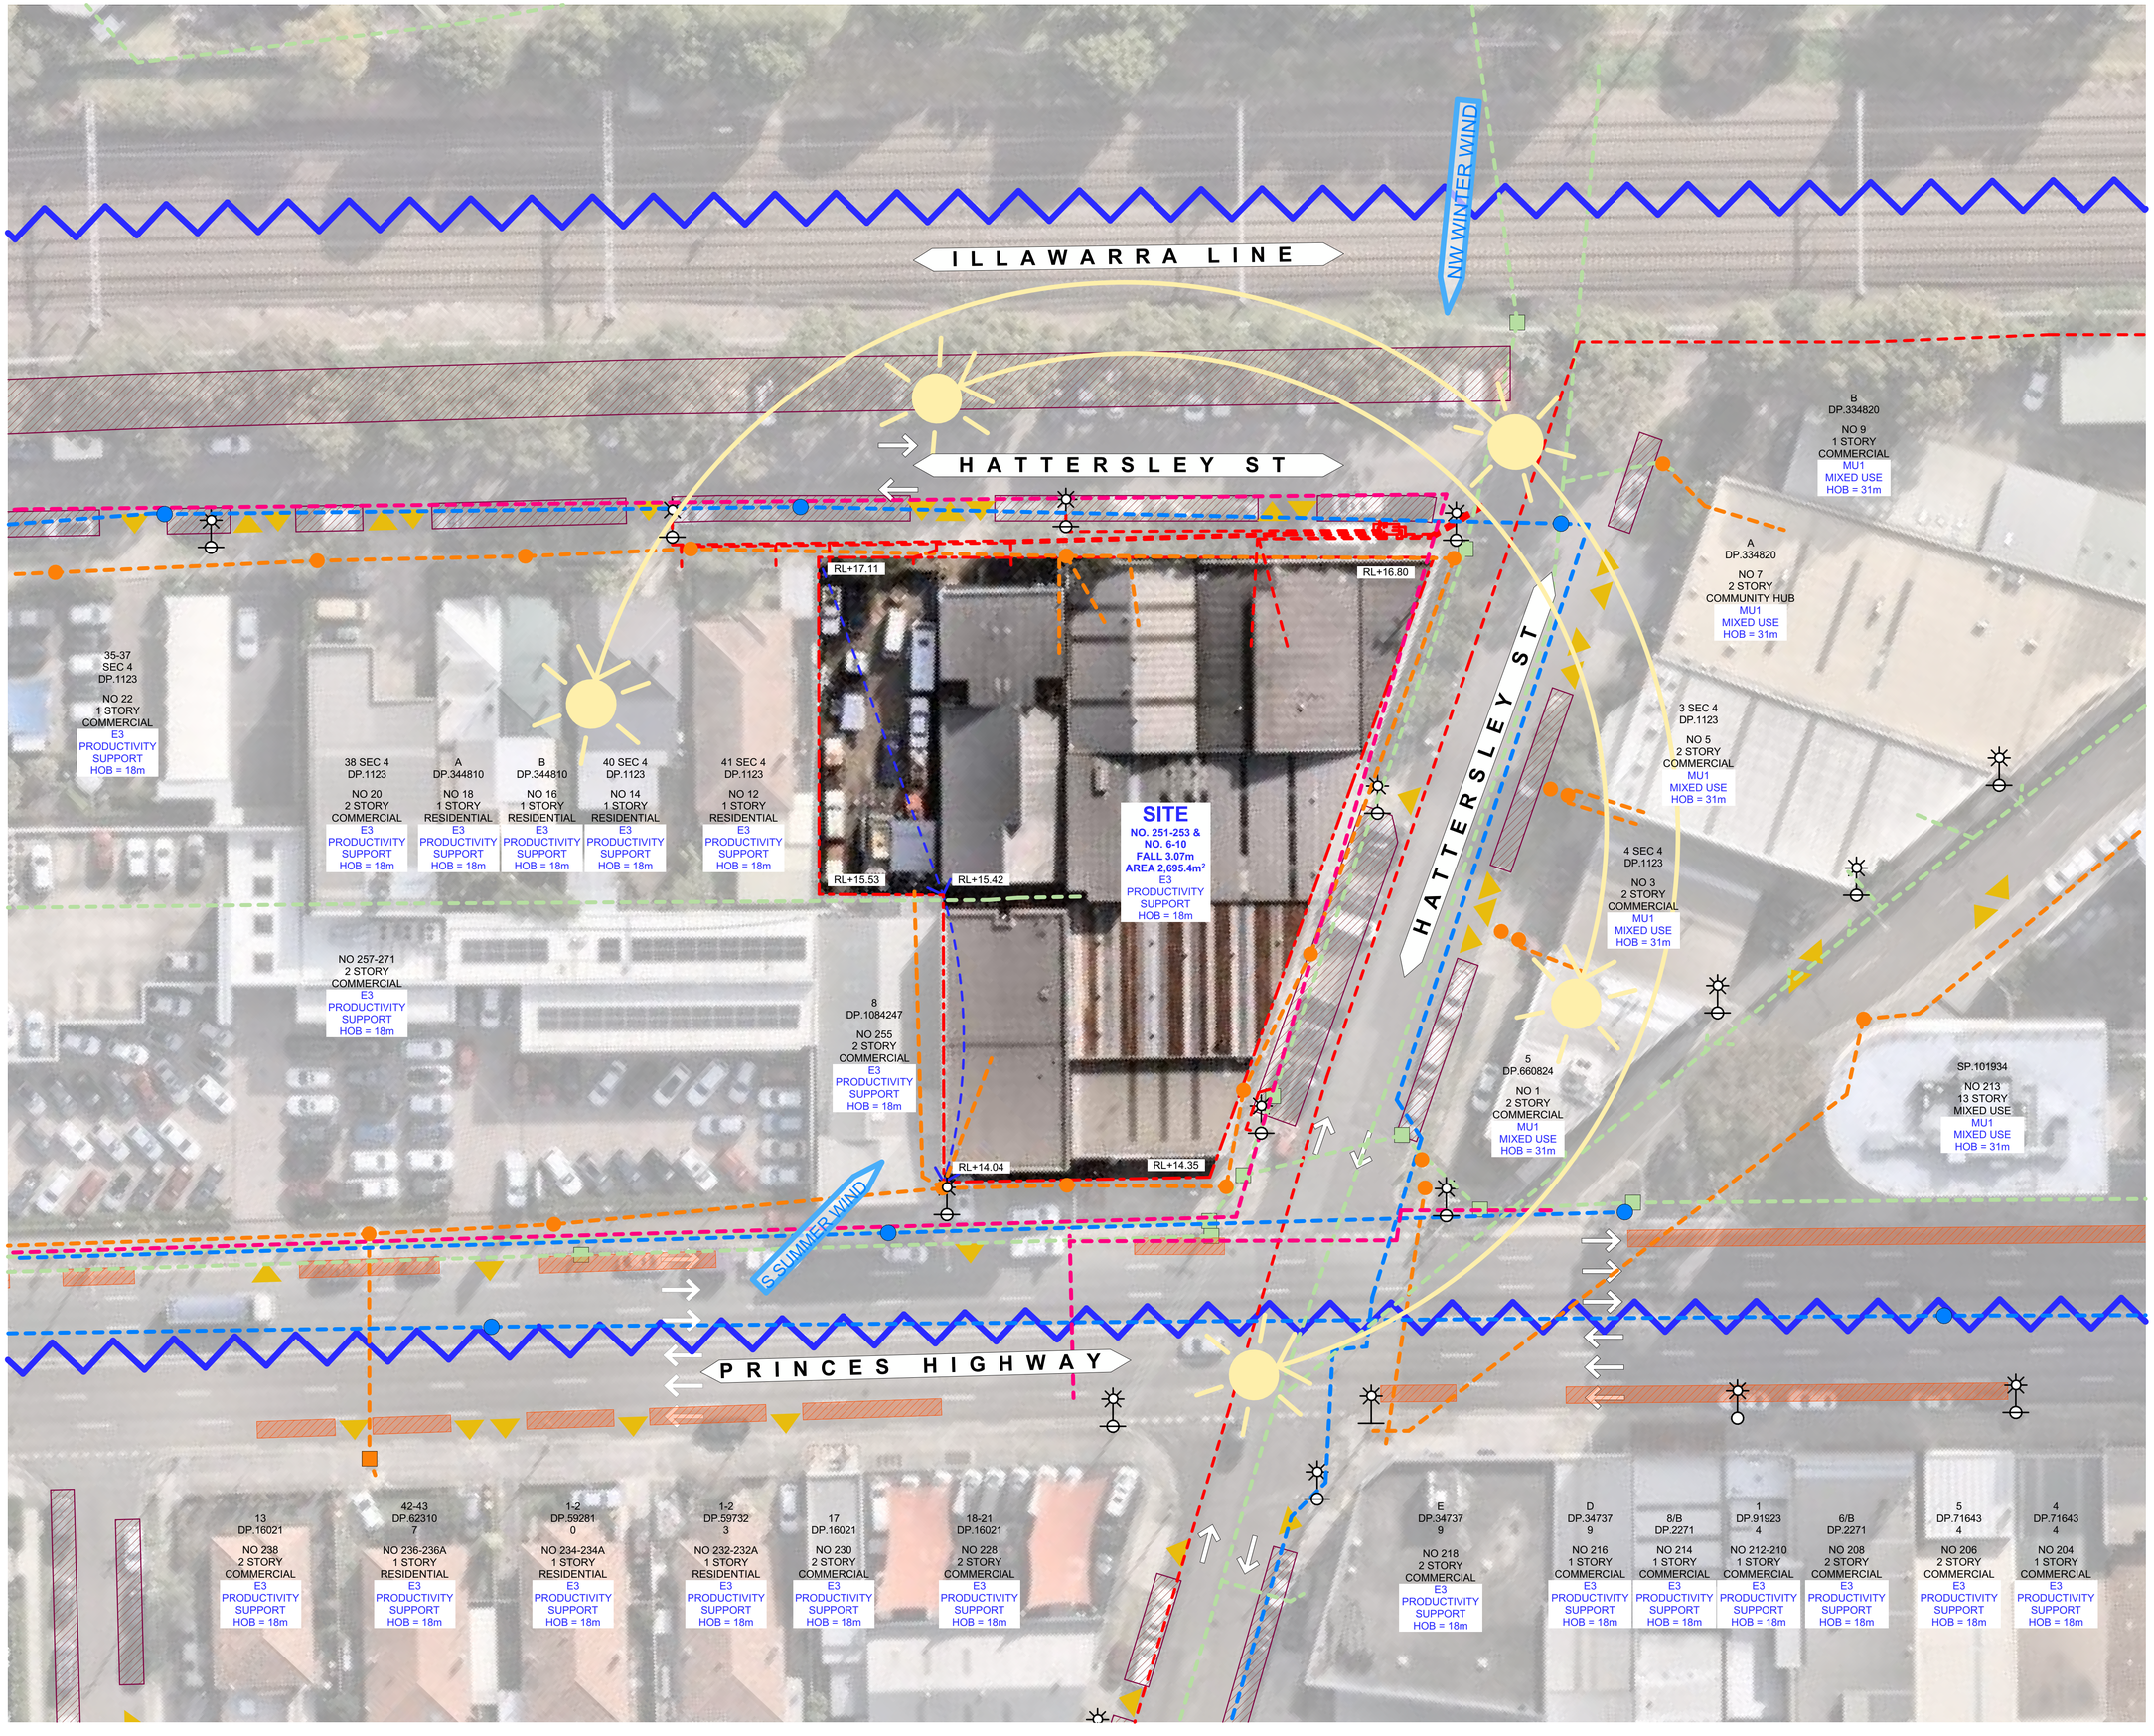


GENERAL NOTES

DA ARCHITECTS.

- NO REPRODUCTION WITHOUT PERMISSION UNLESS NOTED ATHERWISE.
- THIS DRAWING IS NOT FOR CONSTRUCTION.

LEGEND

- SITE
- STREET PARKING ZONE
- STREET PARKING ZONE ON CLEARWAY 6-10AM MON-FRI
- FALL OF TERRAIN
- VEHICULAR ACCESS
- TRAFFIC DIRECTION AND LANES
- LIGHT POLE
- POWER POLE
- PREVAILING BREEZES
- NOISE SOURCE
- ELECTRICAL CONDUITS
- ELECTRICAL CABLES
- POWER LINES
- GAS MAIN
- WATER MAIN
- SEWER MAIN
- HYDRANT
- NBN PIT
- TELSTRA PIT

REVISION ID	AMENDMENT	DATE
A	Issue for Development Application	22/11/2024
C	Amended Development Application	10/04/2025
E	Amended Development Application	26/06/2025
F	Amended Development Application	9/09/2025

ARCHITECT

CLIENT

AARON SUTHERLAND
PO BOX 614,
BOWRAL, NSW 2576

0 3 6 12m

PRELIMINARY

SITE ADDRESS
251-253 PRINCES HWY & 6-10 HATTERSLEY ST, ARNCLIFFE

JOB NO
DA2522

CHECKED	DRAWN	
BD	ZX	
DATE	SCALE	
9/09/2025	1:300 @ A1	A3@50%

PROJECT STATUS
DEVELOPMENT APPLICATION

DRAWING TITLE
SITE ANALYSIS

SHEET NO.	REVISION.
DA 004	F