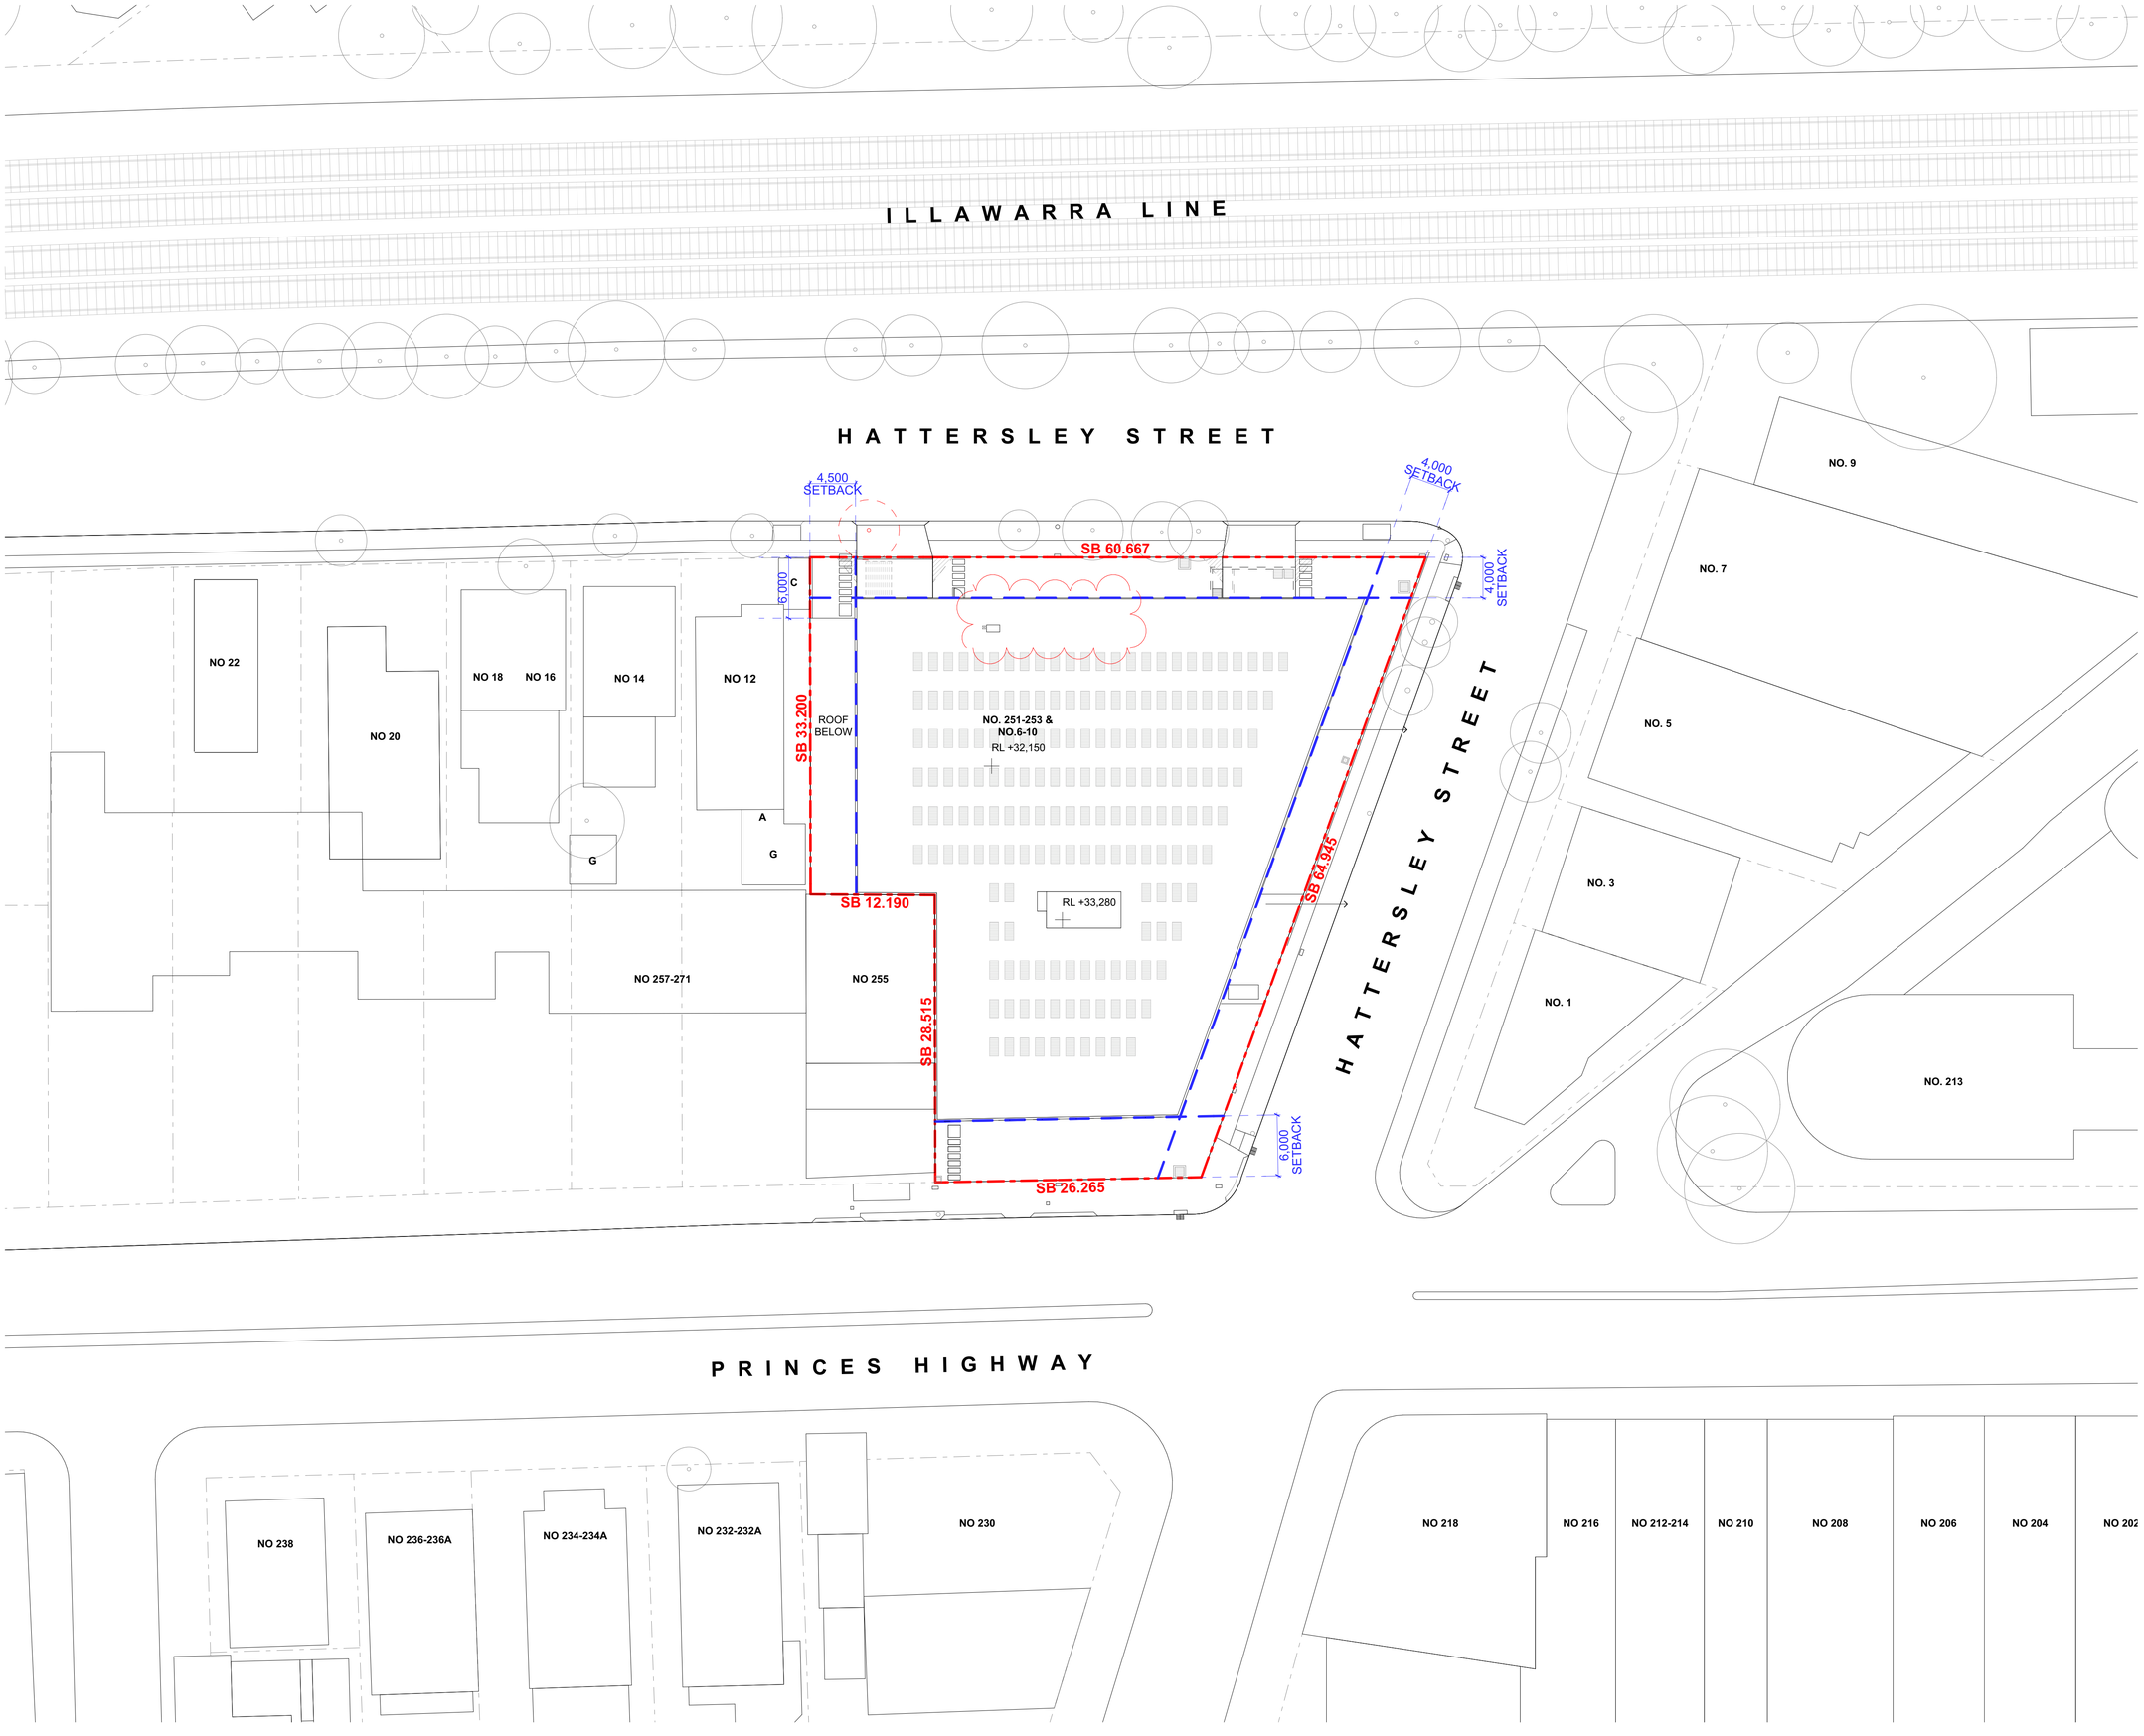


GENERAL NOTES

DA ARCHITECTS.

- NO REPRODUCTION WITHOUT PERMISSION UNLESS NOTED ATHERWISE.
- THIS DRAWING IS NOT FOR CONSTRUCTION.
- ALL DIMENSIONS AND LEVELS ARE TO BE CHECKED ON SITE PRIOR TO THE COMMENCEMENT OF WORK.
- INFORM THE ARCHITECT OF ANY DISCREPANCIES FOR CLARIFICATION BEFORE PROCEEDING WITH WORK.
- DRAWINGS ARE NOT TO BE SCALED.
- USE ONLY FIGURED DIMENSIONS.
- REFER TO CONSULTANT DOCUMENTATION FOR FURTHER INFORMATION.

File: DA2522_ARNCLIFFE
Print date and time: Friday, 12 September 2025 @9:36 AM

LEGEND

SITE BOUNDARY

REVISION ID	AMENDMENT	DATE
A	Issue for Development Application	22/11/2024
C	Amended Development Application	10/04/2025
D	Amended Development Application	6/06/2025
E	Amended Development Application	26/06/2025

ARCHITECT

CLIENT

AARON SUTHERLAND
PO BOX 814,
BOWRAL, NSW 2576

0 3 6 12m

PRELIMINARY

SITE ADDRESS
251-253 PRINCES HWY & 6-10 HATTERSLEY ST, ARNCLIFFE

JOB NO
DA2522

CHECKED BD
DRAWN ZX
DATE 12/09/2025
SCALE 1:300 @ A1 A3@50%

PROJECT STATUS
SECTION 4.55

DRAWING TITLE
SITE PLAN

SHEET NO. DA 005
REVISION. F