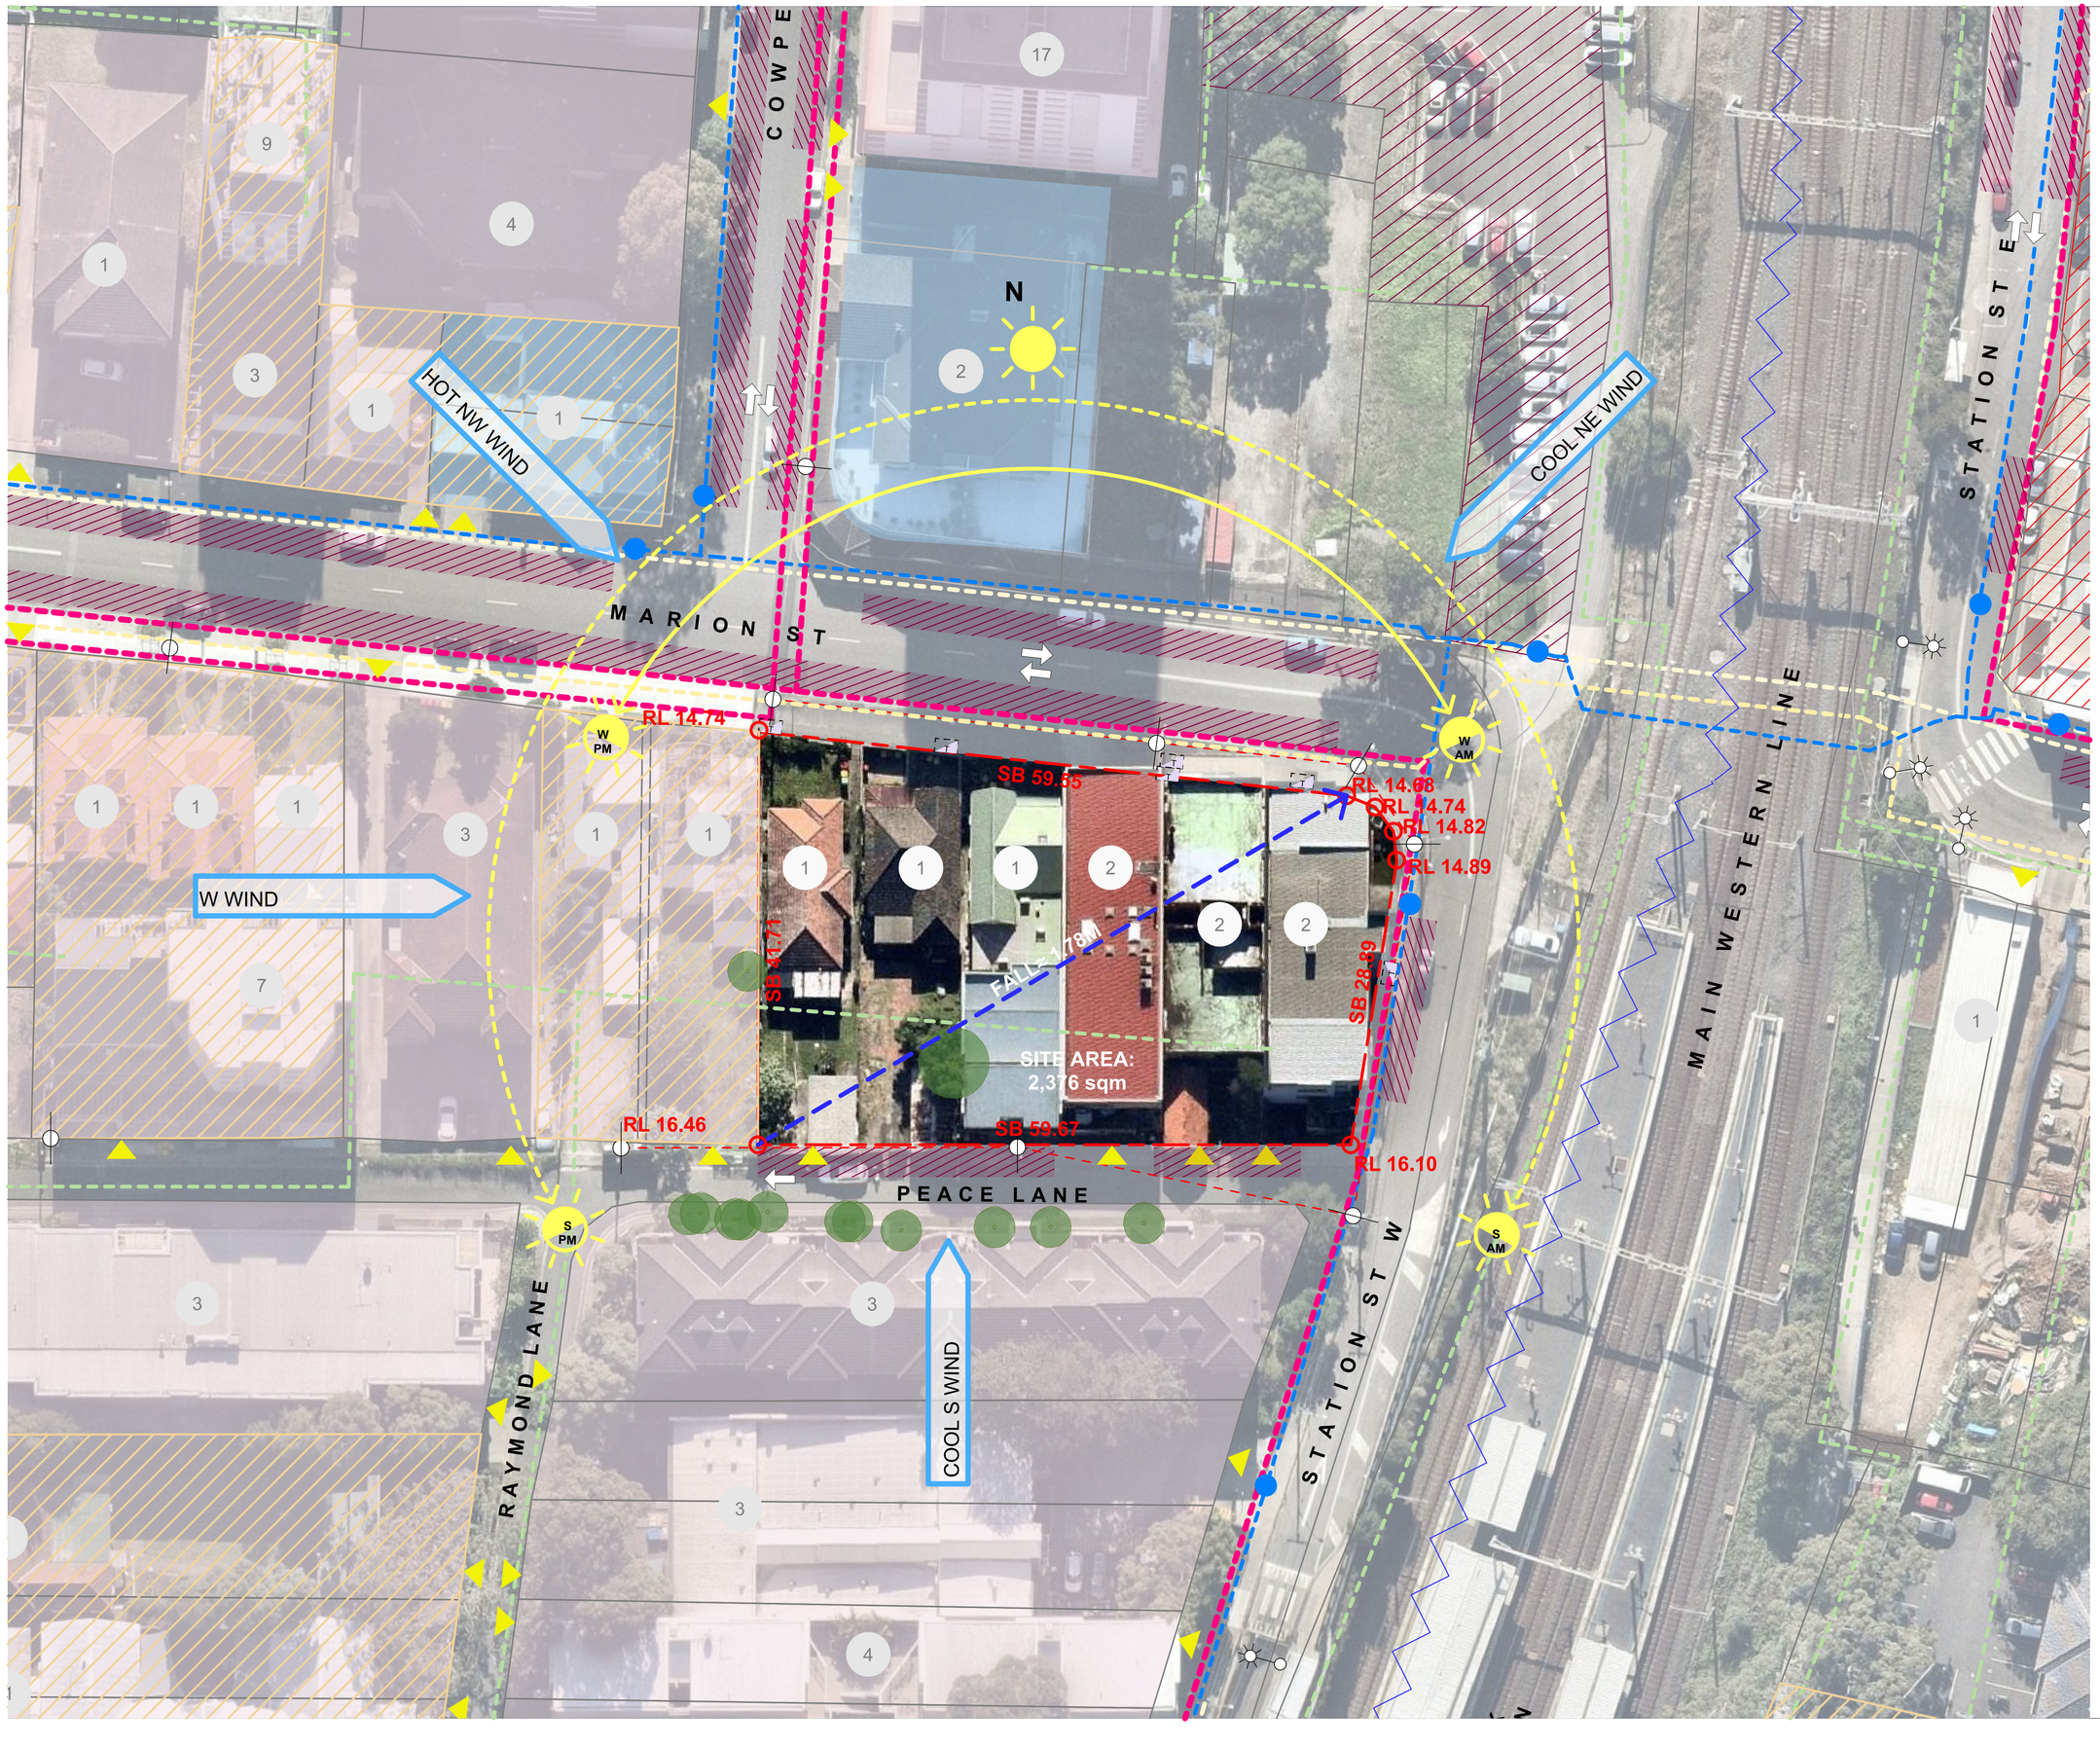


GENERAL NOTES

© FUSE ARCHITECTURE.
•NO REPRODUCTION WITHOUT PERMISSION, UNLESS NOTED OTHERWISE.
•THIS DRAWING IS NOT FOR CONSTRUCTION.
•ALL DIMENSIONS AND LEVELS ARE TO BE CHECKED ON SITE PRIOR TO THE COMMENCEMENT OF WORK.
•SERVICE SPATIALS AND STRUCTURE ARE INDICATIVE ONLY. FINAL DESIGN TO BE DEVELOPED AND PROVIDED THERE IS NO CHANGE TO THE EXTERNAL ENVELOPE THIS WILL BE CONSIDERED CONSISTENT WITH THESE PLANS. DRAWINGS CANNOT BE RELIED UPON FOR THE BASIS OF MARKETING SALES OR CONSTRUCTION QUOTATION.
•INFORM FUSE ARCHITECTURE OF ANY DISCREPANCIES FOR CLARIFICATION BEFORE PROCEEDING WITH WORK.
•DRAWINGS ARE NOT TO BE SCALED.
•USE ONLY FIGURED DIMENSIONS.
•REFER TO CONSULTANT DOCUMENTATION FOR FURTHER INFORMATION.

File: 2504_PARRAMATTA4
Print date and time: Thursday, December 4, 2025 @ 5:11 PM

LEGEND

- SITE
- STREET PARKING ZONE
- FALL OF TERRAIN
- VEHICULAR ACCESS
- TRAFFIC DIRECTION AND LANES
- POWER POLE
- LIGHT POLE
- PREVAILING BREEZES
- NOISE SOURCE
- POWER LINES
- ELECTRICAL LINE
- GAS MAIN
- WATER MAIN
- SEWER MAIN
- HYDRANT
- TELSTRA PIT
- SIGNIFICANT EXISTING TREE CANOPY
- GENERAL HERITAGE SITE
- CONSERVATION AREAS
- MARION STREET CARPARK
- SUN PATH
  S= SUMMER
  W= WINTER
- CURRENT RESIDENTIAL BUILDING
- CURRENT COMMERCIAL BUILDING
- NUMBER OF STORIES

REVISION ID	AMENDMENT	DATE
P1	ISSUE FOR DRP 01	7/25/2025
P2	ISSUE FOR DRP 02	8/12/2025
A	ISSUE FOR SSDA SUBMISSION	12/4/2025

ARCHITECT
FUSE ARCHITECTS
STUDIO 211-212
59 GREAT BUCKINGHAM STREET
REDFERN NSW 2016
MAIL@FUSEARCHITECTURE.COM.AU
PHONE 02 8278 7156
ABN 81 612 046 643
NOMINATED ARCHITECT RACHID ANDARY NSW ARB 8627

CLIENT
CN Marion Pty Ltd
L 2/111 Parramatta Rd
Concord NSW 2137

FOR APPROVAL

N

0 1m 2m 5m 10m

SITE ADDRESS
33-43 MARION STREET PARRAMATTANSW 2150

JOB NO
2504

CHECKED VC/AD
DRAWN JA/KH
DATE APR 2025
SCALE 1:300 @ A1 A3@50%

PROJECT STATUS
STATE SIGNIFICANT DESIGN APPLICATION

DRAWING TITLE
SITE ANALYSIS

SHEET NO. SSDA 004
REVISION. A