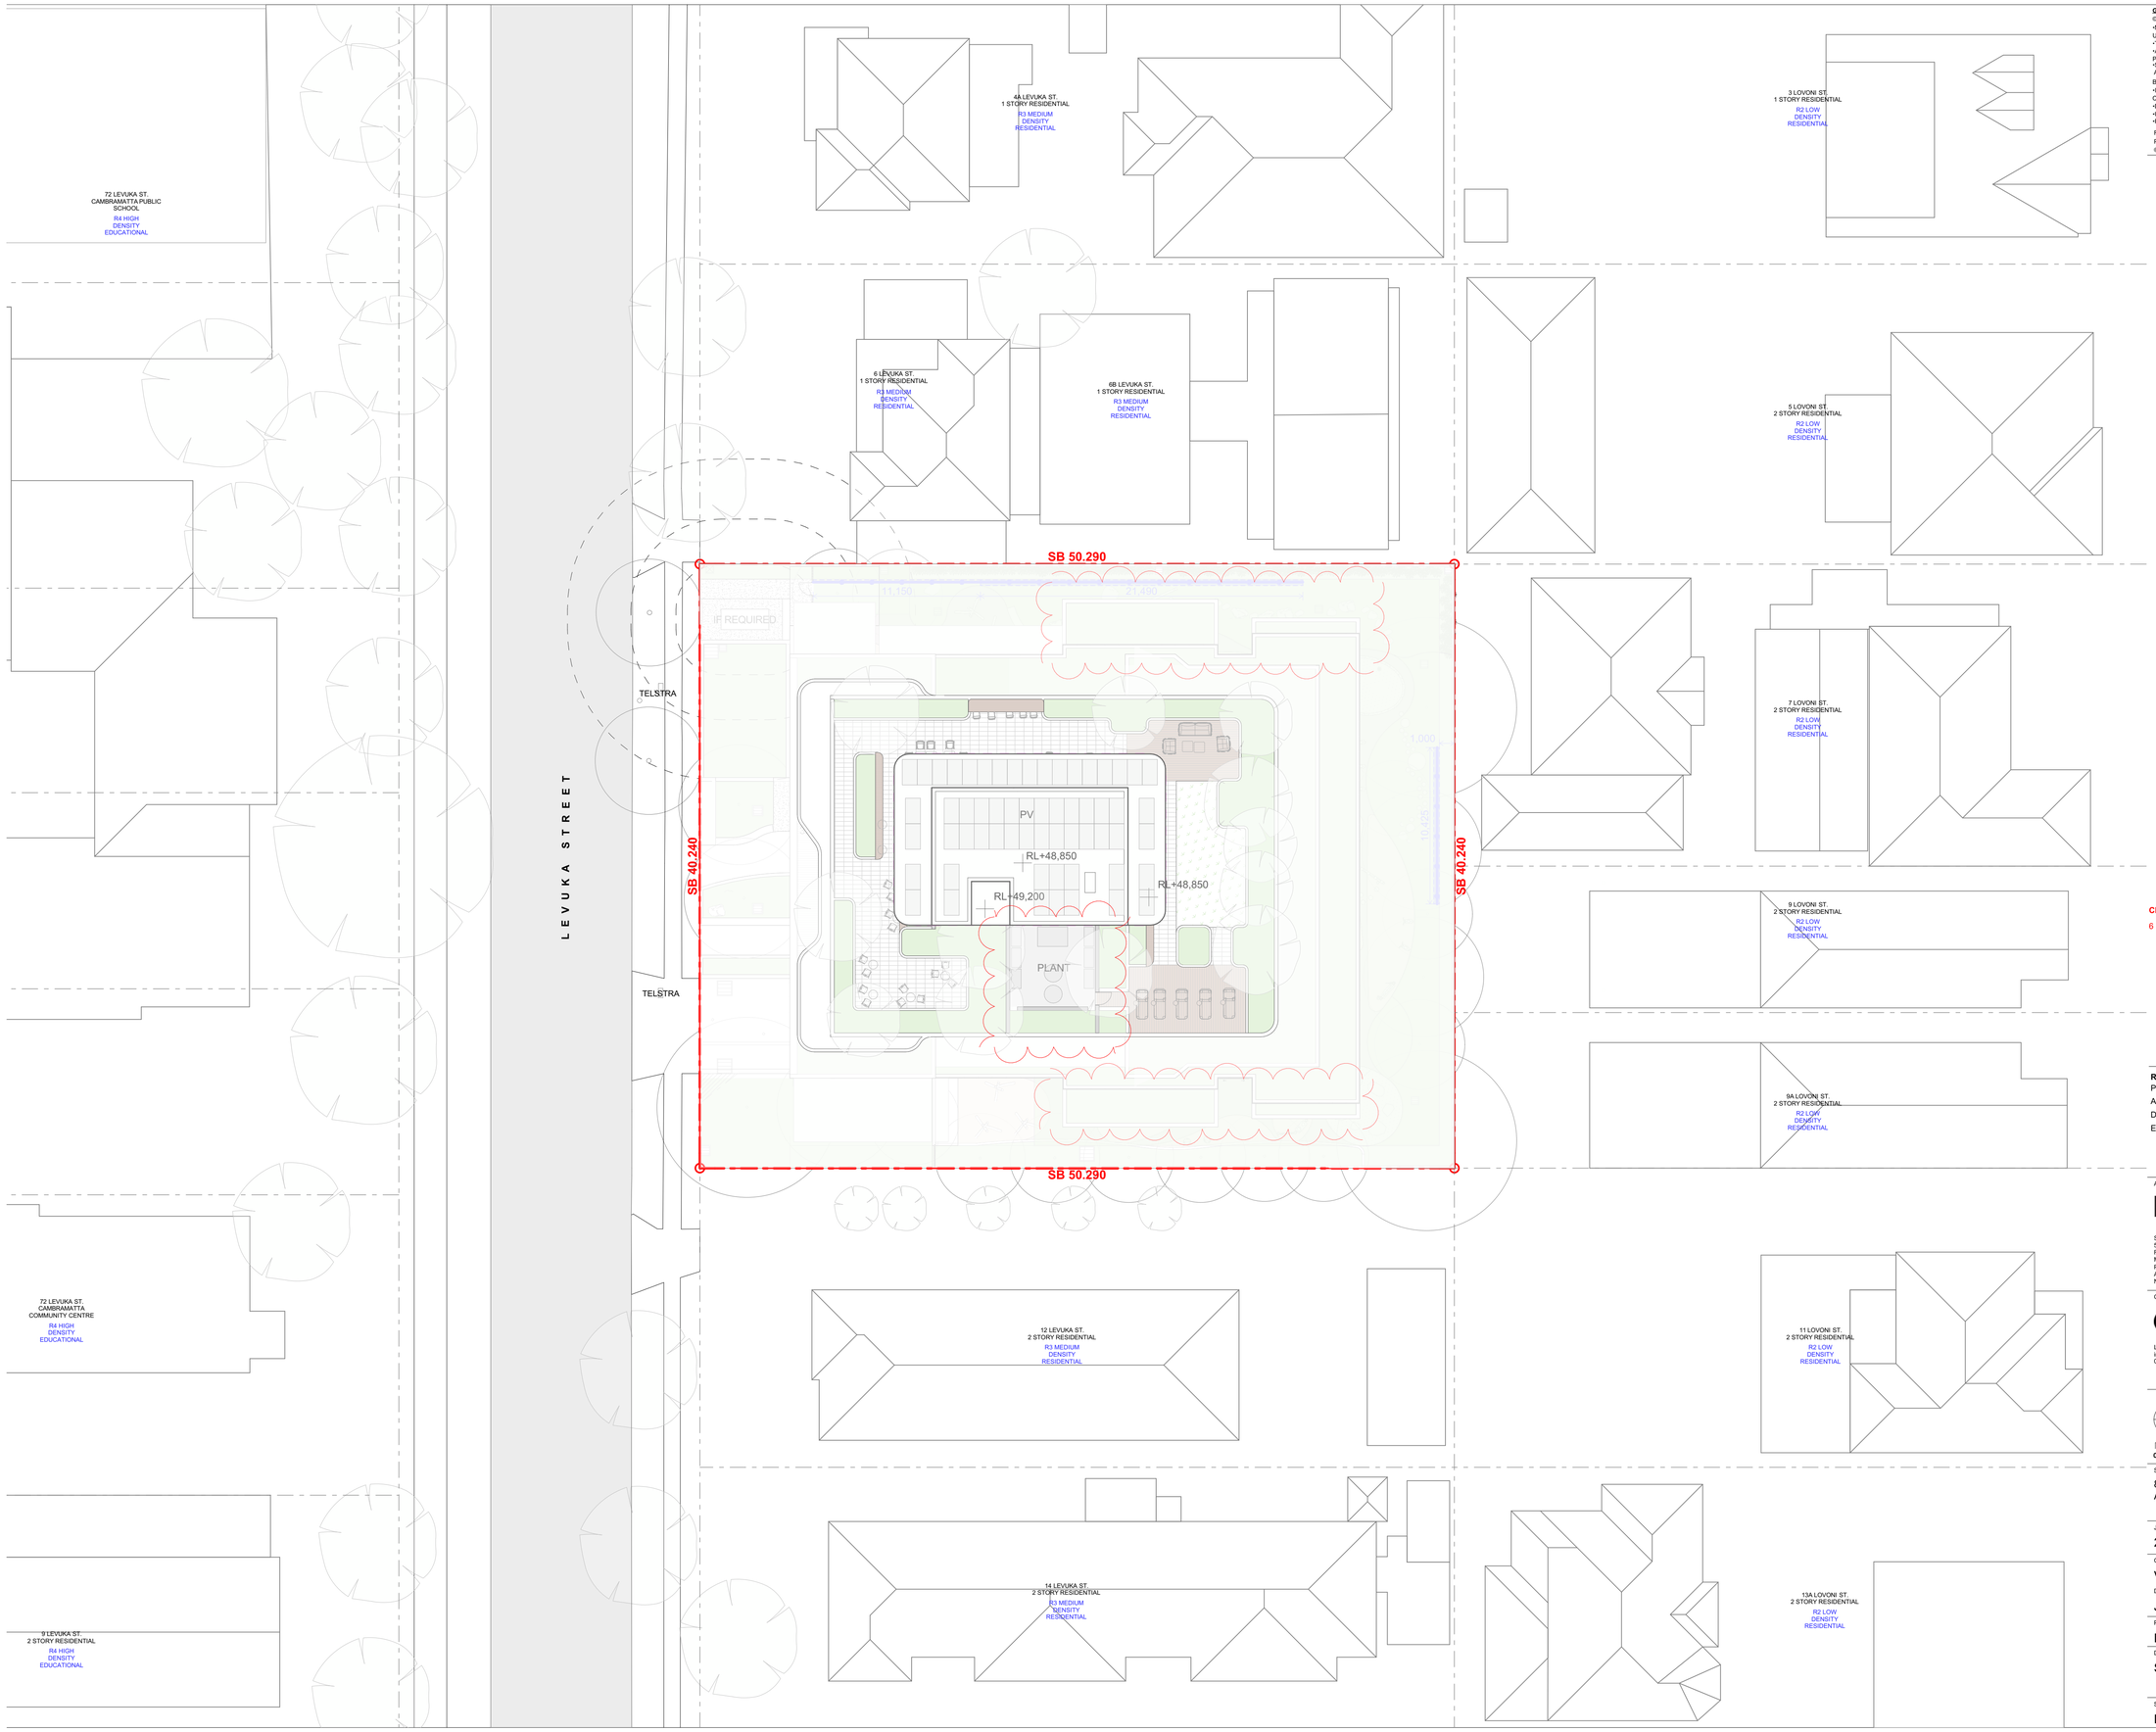



**GENERAL NOTES**

© FUSE ARCHITECTS.
•NO REPRODUCTION WITHOUT PERMISSION
UNLESS NOTED OTHERWISE.
•THIS DRAWING IS NOT FOR CONSTRUCTION.
•ALL DIMENSIONS AND LEVELS ARE TO BE CHECKED ON SITE
PRIOR TO THE COMMENCEMENT OF WORK.
•SERVICES SPATIALS + STRUCTURE ARE INDICATIVE ONLY; FINAL DESIGN TO BE DEVELOPED
AND PROVIDED THERE IS NO CHANGE TO THE EXTERNAL ENVELOPE/COMPLIANCE THIS WILL
BE CONSIDERED CONSISTENT WITH THESE PLANS.
•INFORM FUSE ARCHITECTURE OF ANY •DISCREPANCIES FOR
CLARIFICATION BEFORE PROCEEDING WITH WORK.
•DRAWINGS ARE NOT TO BE SCALED.
•USE ONLY FIGURED DIMENSIONS.
•REFER TO CONSULTANT DOCUMENTATION FOR FURTHER INFORMATION.

File: 2509_CABRAMATTA1
Print date and time: Thursday, 16 July 2026 @ 9:32 AM
© FUSE ARCHITECTS.

| CHANGE | DESCRIPTION |
|---|---|
| 6 | AMENDMENT TO ROOF PLANT LAYOUT AND ACOUSTIC BARRIER |

| REVISION ID | AMENDMENT | DATE |
|---|---|---|
| P1 | ISSUE FOR COORDINATION | 3/10/2025 |
| A | DEVELOPMENT APPLICATION | 27/10/2025 |
| D | DEVELOPMENT APPLICATION | 29/05/2026 |
| E | DEVELOPMENT APPLICATION | 15/07/2026 |

ARCHITECT
FUSE ARCHITECTS
STUDIO 212
59 GREAT BUCKINGHAM STREET
REDFERN NSW 2016
MAIL@FUSEARCHITECTURE.COM.AU
PHONE 02 8278 7158
ABN 81 612 046 643
NOMINATED ARCHITECT RACHID ANDARY NSW ARB 8627

CLIENT
CHEGO
Levuka Developments
info@chego.com.au
0424 305 085

N
0 2 5 10m

SITE ADDRESS
8 & 10 LEVUKA STREET, CABRAMATTA NSW 2166
AUSTRALIA

JOB NO
2509

| CHECKED | DRAWN |
|---|---|
| VC/GA | EQ/KT |
| DATE | SCALE |
| JUN 2025 | 1:200 @ A1 A3@50% |

PROJECT STATUS
DEVELOPMENT APPLICATION

DRAWING TITLE
SITE PLAN

| SHEET NO. | REVISION. |
|---|---|
| DA 005 | E |