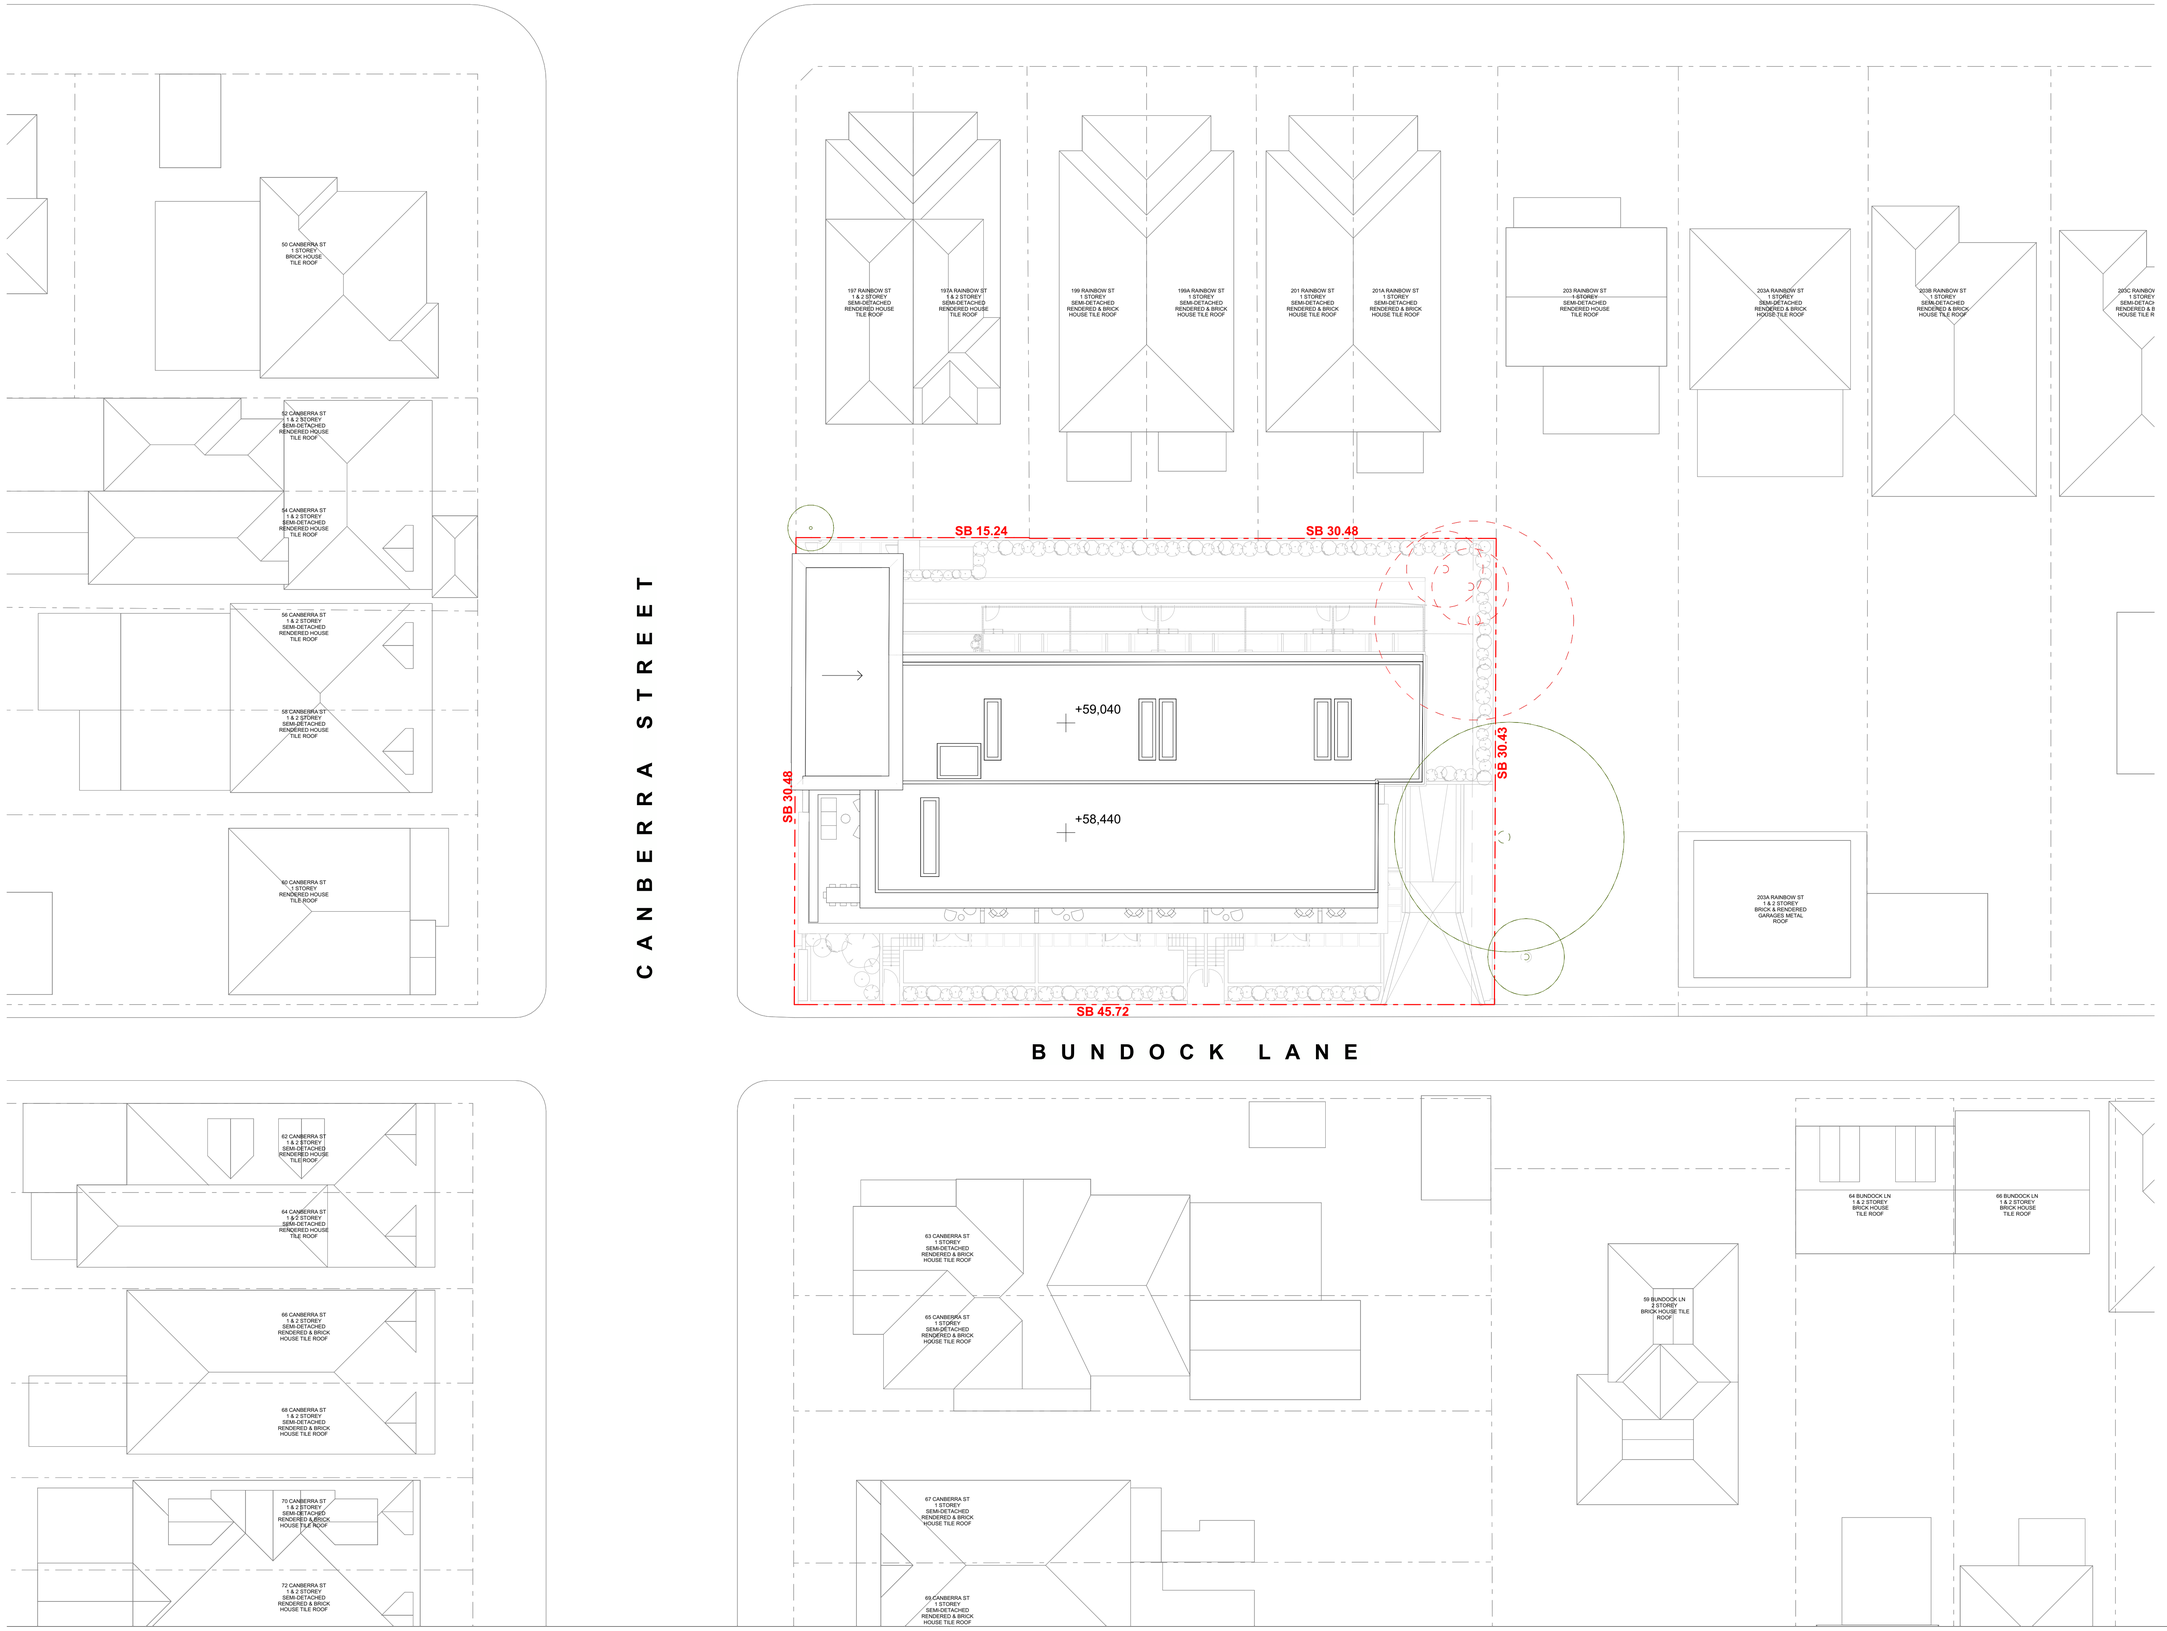


File: 2520_RANDWICK
Print date and time: Tuesday, 25 November 2025 @ 2:48 PM

© FUSE ARCHITECTURE.
NOTE:

- NO REPRODUCTION WITHOUT PERMISSION, UNLESS NOTED OTHERWISE.
- THIS DRAWING IS NOT FOR CONSTRUCTION.
- NO STRUCTURAL OR SERVICE ENGINEERING INPUT OR COORDINATION HAS BEEN PROVIDED IN THE PREPARATION OF THE DRAWINGS. DRAWINGS CANNOT BE RELIED UPON FOR THE BASIS OF MARKETING SALES OR CONSTRUCTION QUOTATION.
- ALL DIMENSIONS AND LEVELS ARE TO BE CHECKED ON SITE PRIOR TO THE COMMENCEMENT OF WORK.
- INFORM FUSE ARCHITECTURE OF ANY DISCREPANCIES FOR CLARIFICATION BEFORE PROCEEDING WITH WORK.
- DRAWINGS ARE NOT TO BE SCALED.
- USE ONLY FIGURED DIMENSIONS.
- REFER TO CONSULTANT DOCUMENTATION FOR FURTHER INFORMATION.

LEGEND

EXISTING TREE RETAINED

EXISTING TREE REMOVED

CHANGE DESCRIPTION

REVISION ID	AMENDMENT	DATE
A	PLANNING PROPOSAL	5/11/2025

ARCHITECT
FUSE—ARCHITECTS
STUDIO 212—59
GREAT BUCKINGHAM STREET
REDFERN NSW 2016
MAIL@FUSEARCHITECTURE.COM.AU
PHONE 02 8278 7156
ABN 81 612 046 643
NOMINATED ARCHITECT RACHID ANDARY NSW ARB 8627

CLIENT
AURORA PROPERTY PARTNERSHIP
24-28 CAMPBELL STREET
SYDNEY NSW 2000

N
0 2 5 10m

SITE ADDRESS
55-61 CANBERRA ST RANDWICK NSW 2031

JOB NO
2520

CHECKED	DRAWN	
PI	TT/YJ	
DATE	SCALE	
JUN 2025	1:200 @ A1	A3@50%

PROJECT STATUS
CONCEPT DESIGN

DRAWING TITLE
SITE PLAN

SHEET NO.	REVISION.
DA 005	A