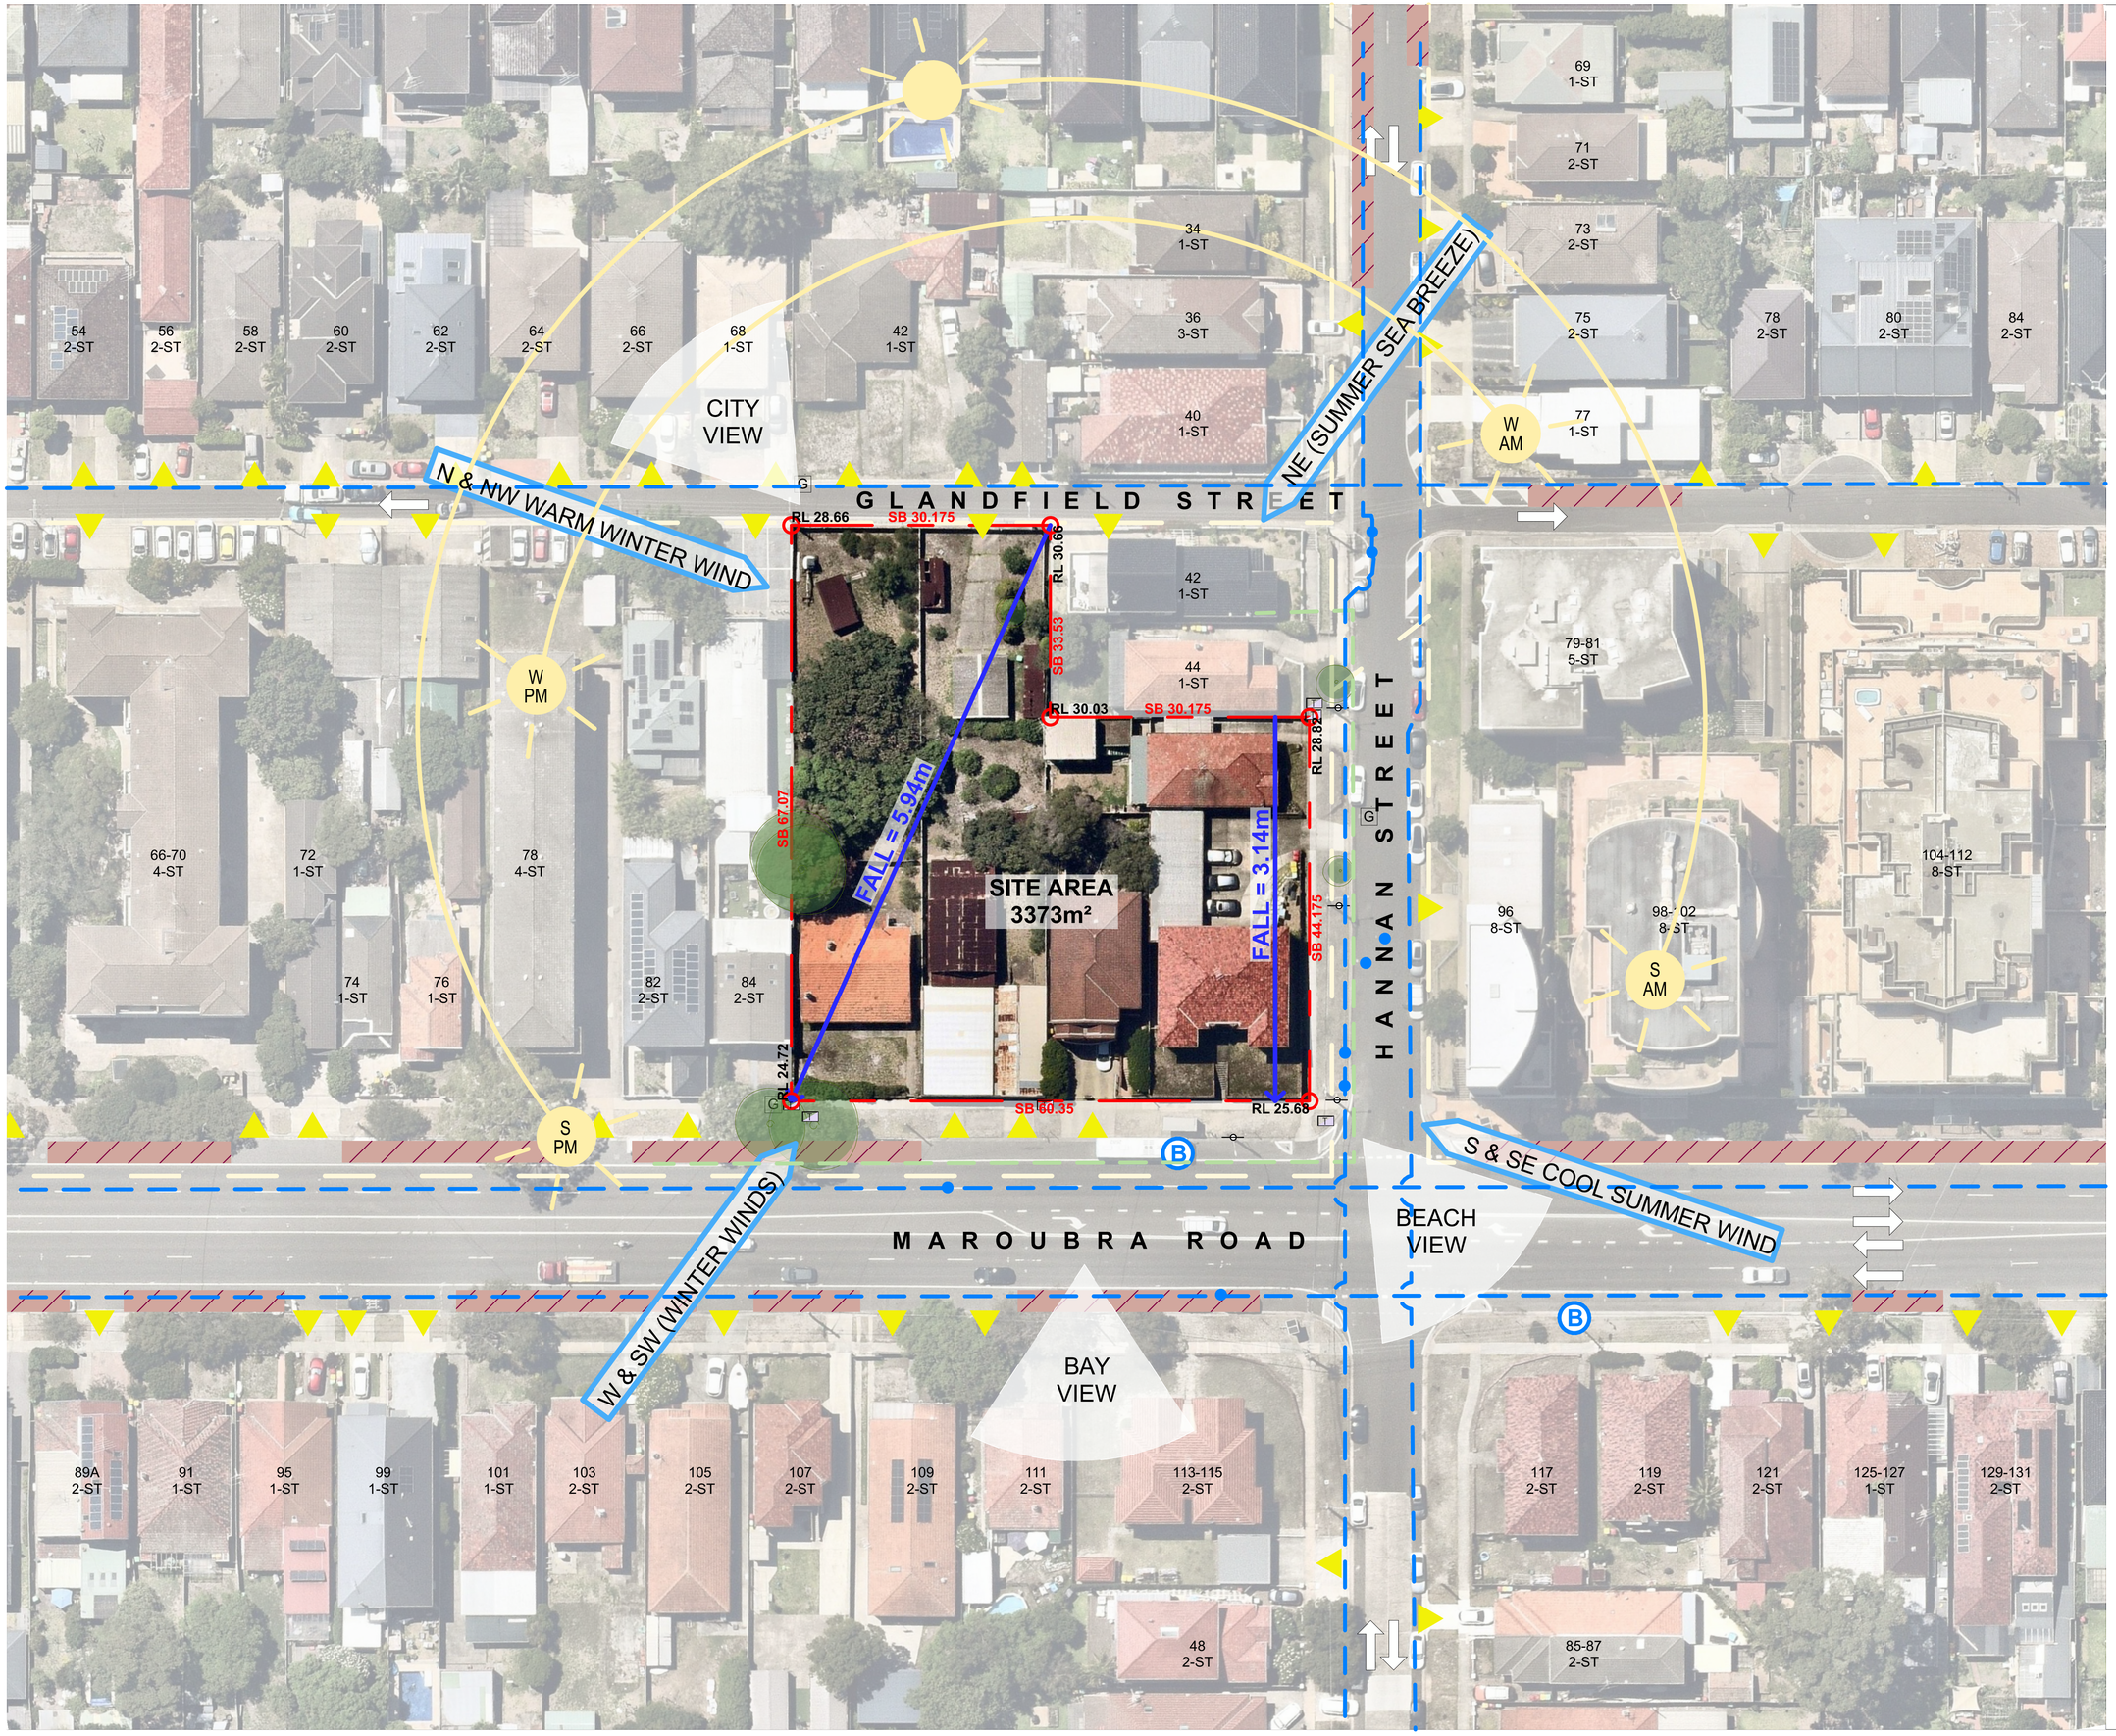


File: 2524_Maroubra_86-90 Maroubra Rd_SSDA_Layout_01
Print date and time: Saturday, June 20, 2026 @ 8:12 AM
© FUSE ARCHITECTURE.
NOTE:

LEGEND

- SITE
- STREET PARKING ZONE
- FALL OF TERRAIN
- VEHICULAR ACCESS
- TRAFFIC DIRECTION AND LANES
- POWER POLE
- PREVAILING BREEZES
- WINTER MORNING
- WINTER AFTERNOON
- SUMMER MORNING
- SUMMER AFTERNOON
- POWER LINES
- WATER MAIN
- SEWER MAIN
- HYDRANT
- TELSTRA PIT
- GAS
- BUS STOPS

ISSUE	DESCRIPTION	DATE

ARCHITECT
FUSE ARCHITECTS
STUDIO 212
59 GREAT BUCKINGHAM STREET
REDFERN NSW 2016
MAIL@FUSEARCHITECTURE.COM.AU
PHONE 02 8278 7156
ABN 81 612 046 643
NOMINATED ARCHITECT RACHID ANDARY NSW ARB 8627

CLIENT
H Built Construction
PO BOX 350
Rosebery NSW 2018

PRELIMINARY

N
0 2 5 10m

SITE ADDRESS
86-90 Maroubra Road Maroubra NSW 2524 Australia

JOB NO
2524

CHECKED AC | DRAWN AS

DATE #Project Date | SCALE 1:350 @ A1 | A3@50%

PROJECT STATUS
PRELIMINARY

DRAWING TITLE
SITE ANALYSIS

SHEET NO. SSDA 005 | REVISION.