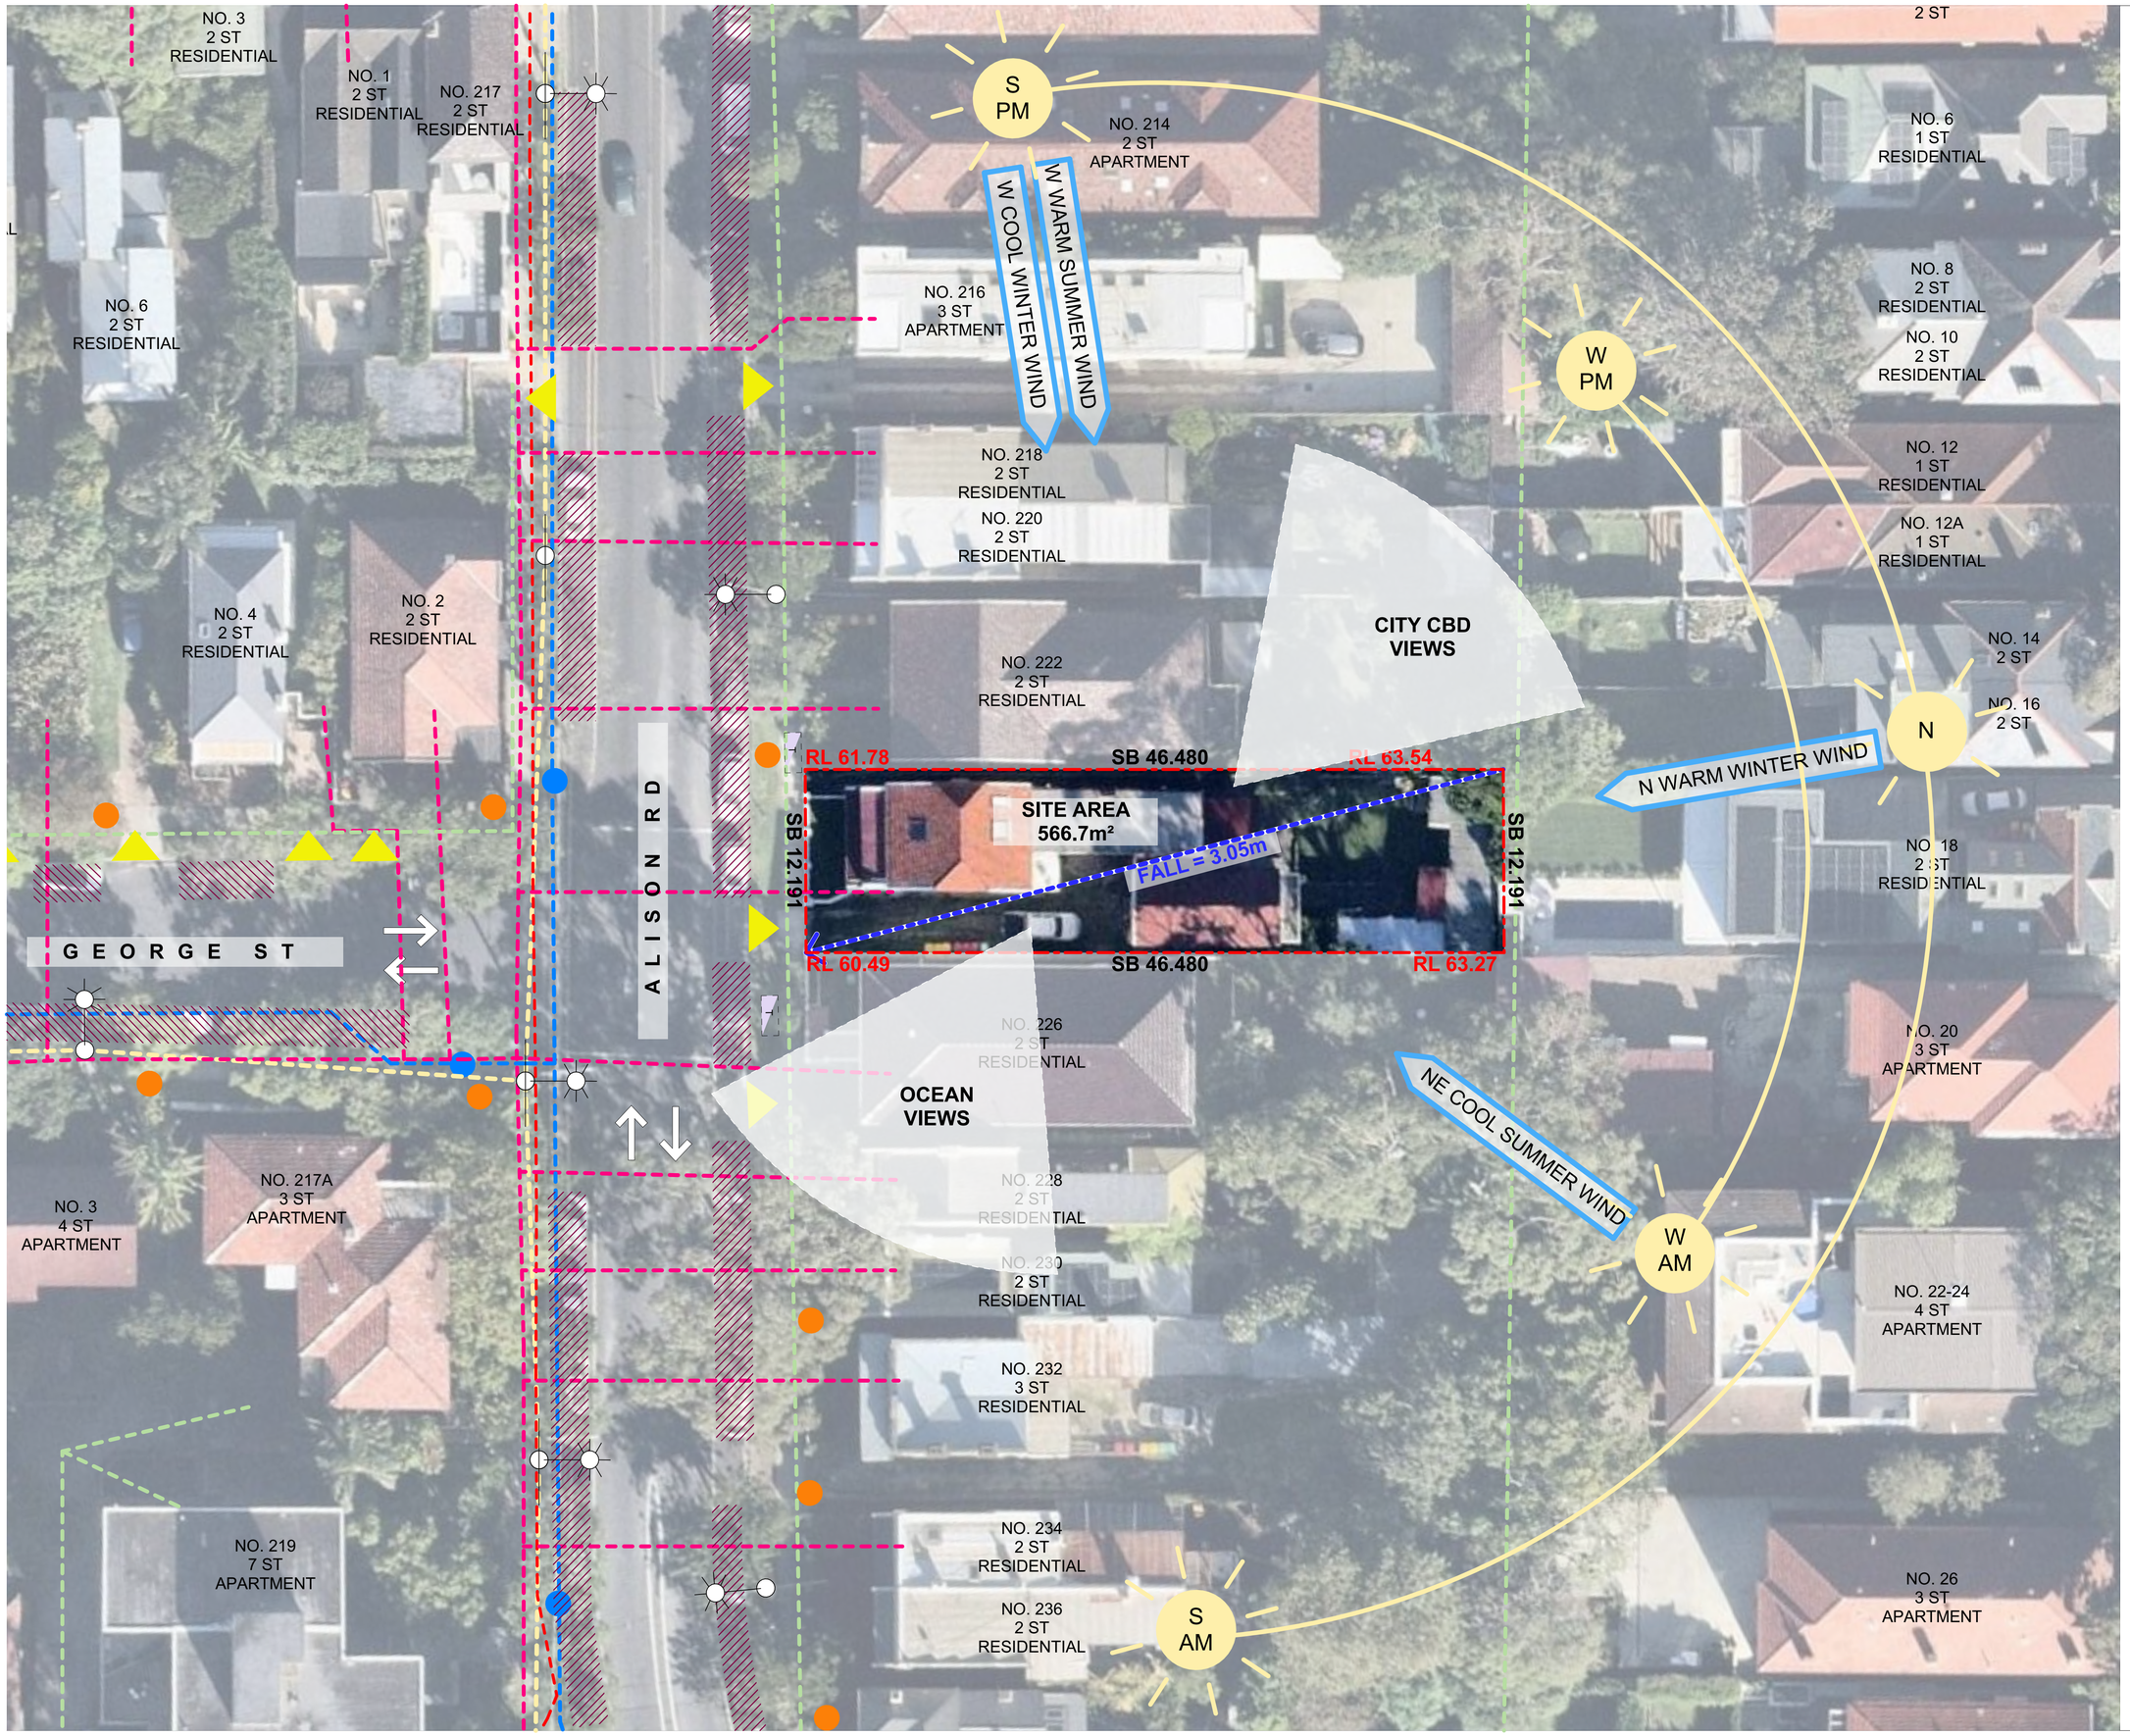


File: 2612_RANDWICK2
Print date and time: Friday, 26 June 2026 @ 9:56 AM

© FUSE ARCHITECTURE.
NOTE:
• NO REPRODUCTION WITHOUT PERMISSION. UNLESS NOTED OTHERWISE.
• THIS DRAWING IS NOT FOR CONSTRUCTION.
• NO STRUCTURAL OR SERVICE ENGINEERING INPUT OR COORDINATION HAS BEEN PROVIDED IN THE PREPARATION OF THE DRAWINGS. DRAWINGS CANNOT BE RELIED UPON FOR THE BASIS OF MARKETING SALES OR CONSTRUCTION QUOTATION.
• ALL DIMENSIONS AND LEVELS ARE TO BE CHECKED ON SITE PRIOR TO THE COMMENCEMENT OF WORK.
• INFORM FUSE ARCHITECTURE OF ANY DISCREPANCIES FOR CLARIFICATION BEFORE PROCEEDING WITH WORK.
• DRAWINGS ARE NOT TO BE SCALED.
• USE ONLY FIGURED DIMENSIONS.
• REFER TO CONSULTANT DOCUMENTATION FOR FURTHER INFORMATION.

LEGEND

- SITE
- STREET PARKING ZONE
- FALL OF TERRAIN
- VEHICULAR ACCESS
- TRAFFIC DIRECTION AND LANES
- LIGHT POLE
- POWER POLE
- PREVAILING BREEZES
- ELECTRICAL CONDUITS
- ELECTRICAL CABLES
- POWER LINES
- GAS MAIN
- WATER MAIN
- SEWER MAIN
- HYDRANT
- NBN PIT
- T — TELSTRA PIT

ISSUE	DESCRIPTION	DATE
P1	ISSUE FOR COORDINATION	16/06/2026
P2	ISSUE FOR COORDINATION	26/06/2026

ARCHITECT
FUSE—ARCHITECTS
STUDIO 212
59 GREAT BUCKINGHAM STREET
REDFERN NSW 2016
MAIL@FUSEARCHITECTURE.COM.AU
PHONE 02 8278 7156
ABN 81 612 046 643
NOMINATED ARCHITECT RACHID ANDARY NSW ARB 8627

CLIENT
H Built
54 MARY STREET
HUNTERS HILL NSW 2110

PRELIMINARY

N

0 2 5 10m

SITE ADDRESS
224 ALISON ROAD
RANDWICK NSW 2031

JOB NO
2612

CHECKED: AC
DRAWN: KT
DATE: MAY 2026
SCALE: 1:200 @ A1 A3@50%

PROJECT STATUS
DEVELOPMENT APPLICATION

DRAWING TITLE
SITE ANALYSIS

SHEET NO. DA 004
REVISION. P2