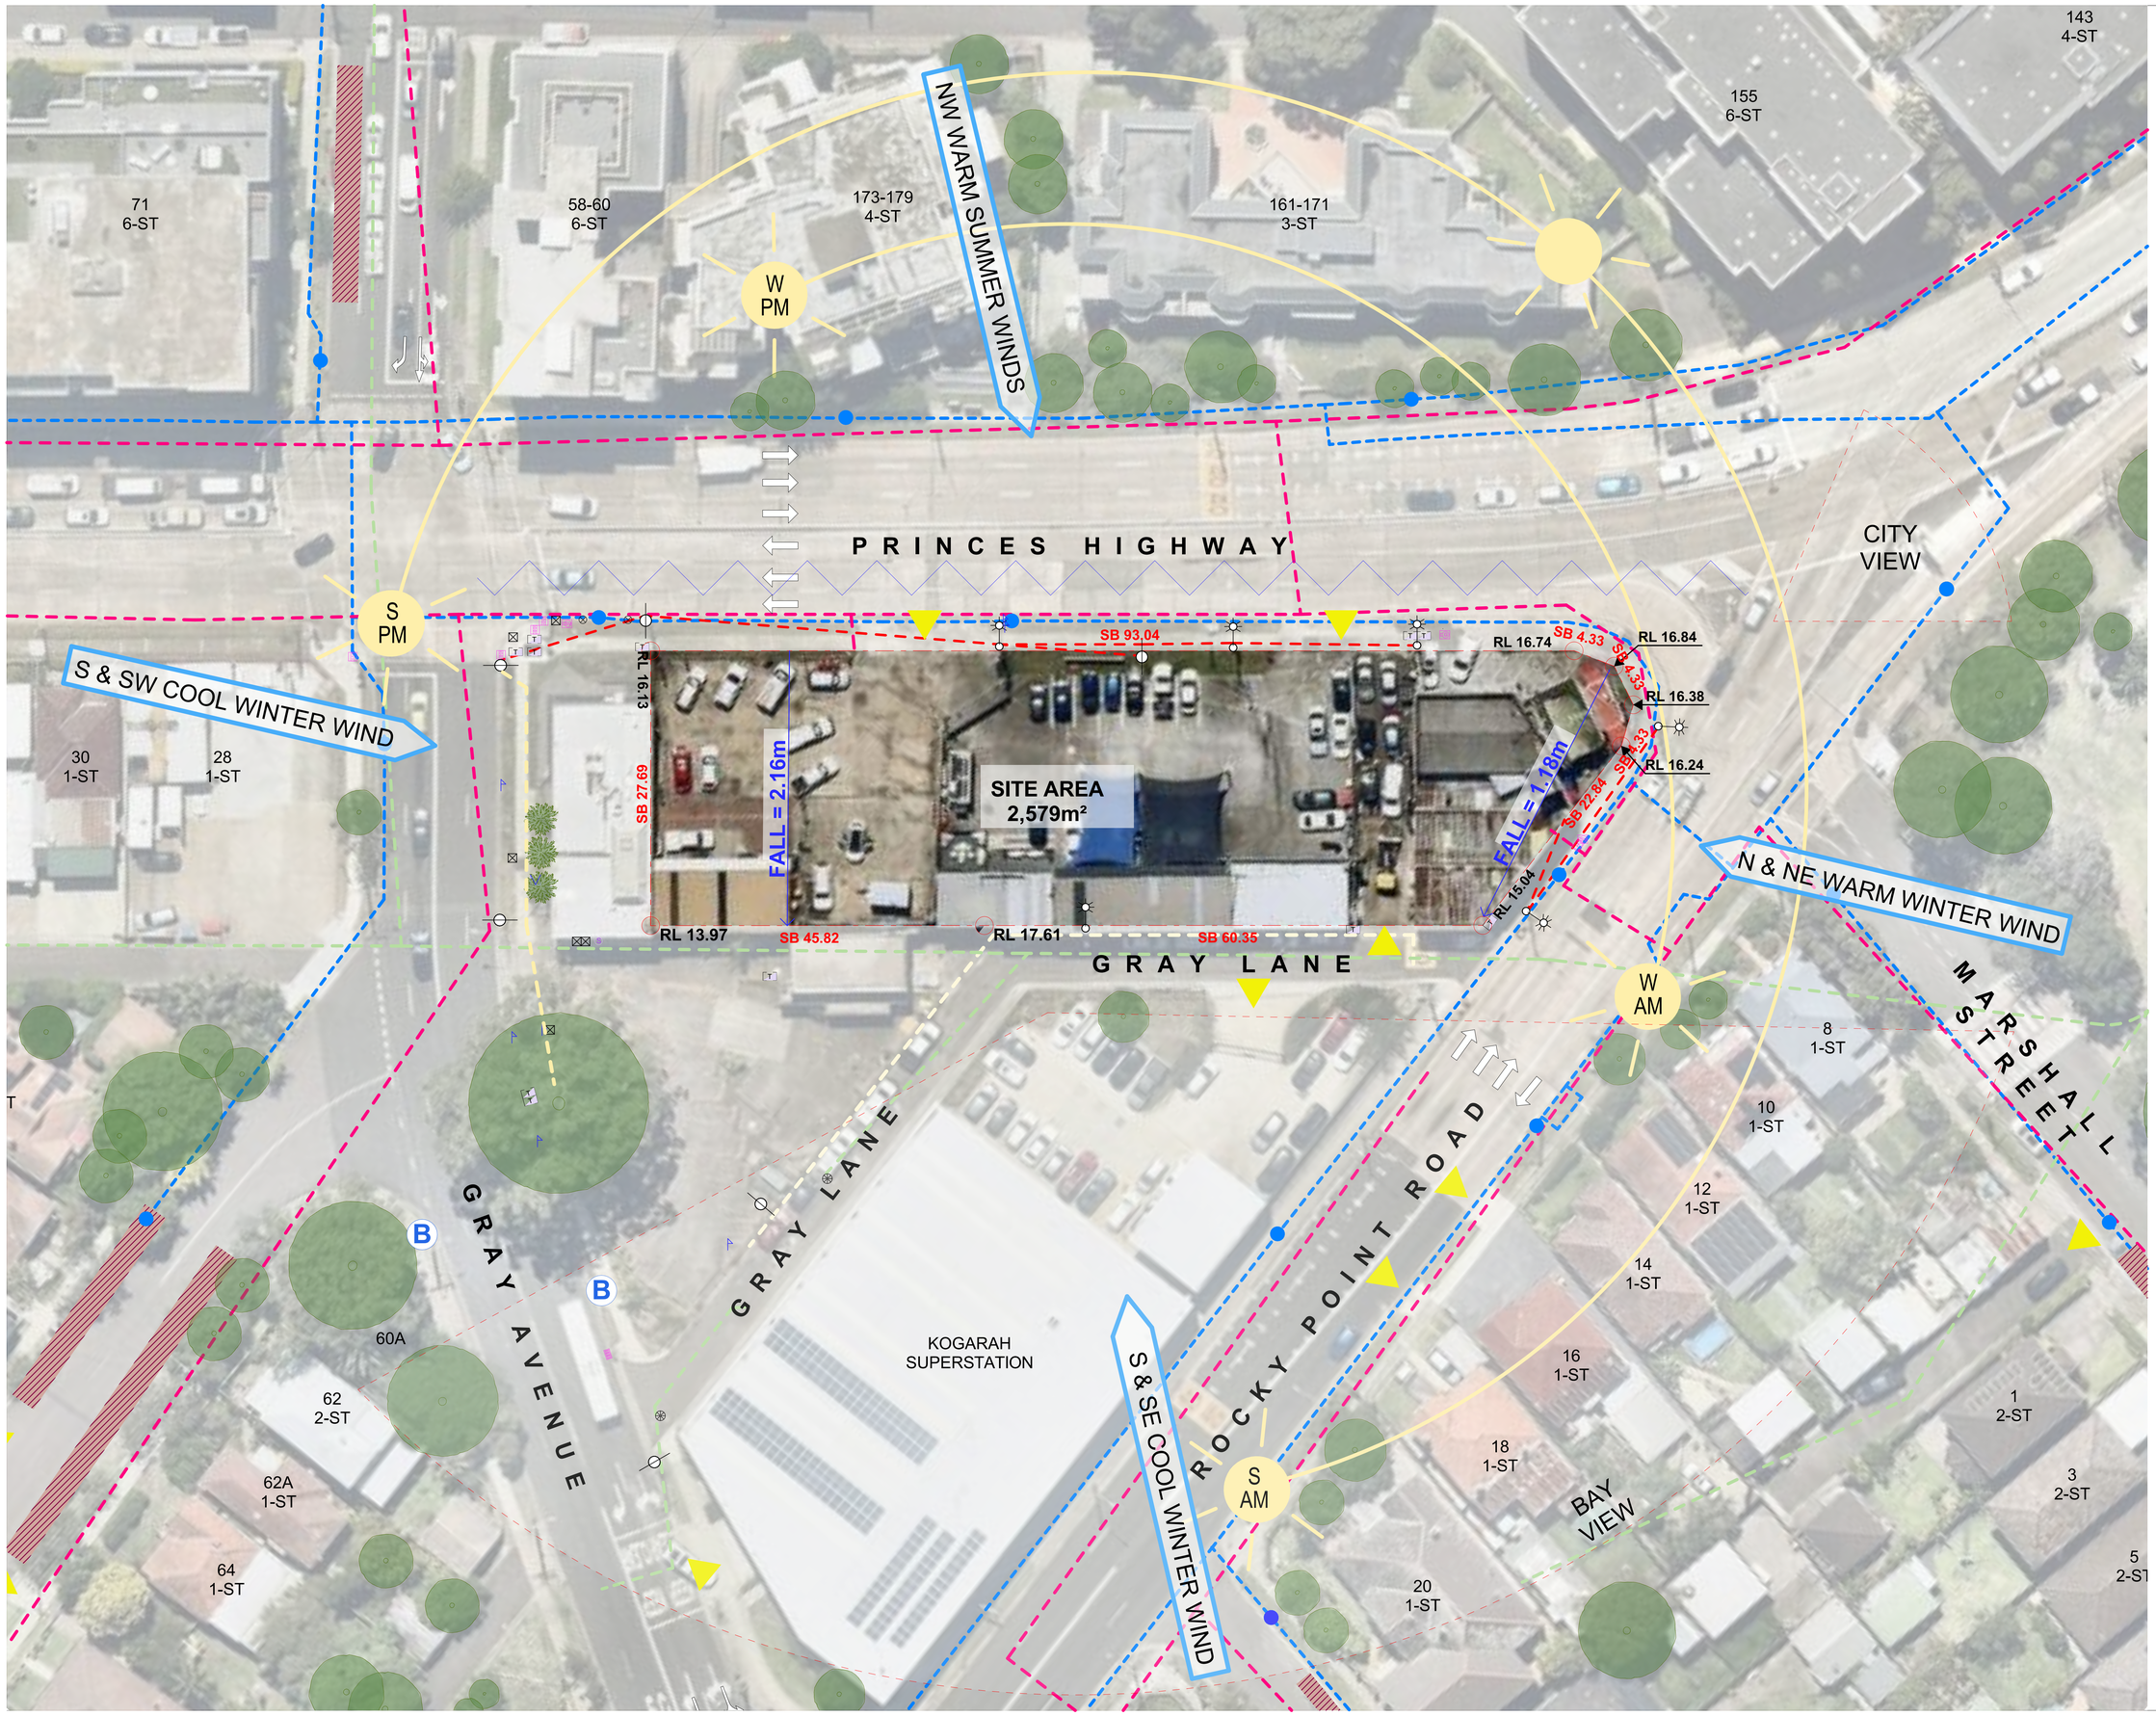


File: 2614_Kogarah_ 18-24 Princes Hwy_ SSDA 01
Print date and time: Monday, 3 August 2026 @ 8:49 PM
© FUSE ARCHITECTURE.
NOTE.

LEGEND

- SITE
- STREET PARKING ZONE
- FALL OF TERRAIN
- VEHICULAR ACCESS
- TRAFFIC DIRECTION AND LANES
- LIGHT POLE
- PREVAILING BREEZES
- SUN PATH (S= SUMMER W= WINTER)
- NOISE SOURCE
- TELSTRA PIT
- SB — SITE BOUNDARY
- ELECTRIC POLE
- ELECTRICAL CABLES
- POWER LINES
- GAS MAIN
- WATER MAIN
- SEWER MAIN
- HYDRANT
- GAS TAP/ VALVE
- STOP VALVE
- BOUNDARY TRAP
- BUS STOPS
- SIGNPOST
- SPEED CAMERA
- SEWER MAN-HOLE
- DRAINAGE PIT
- TRAFFIC SIGNAL POST
- UNKNOWN PIT

ISSUE	DESCRIPTION	DATE

ARCHITECT
FUSE ARCHITECTS
STUDIO 212
59 GREAT BUCKINGHAM STREET
REDFERN NSW 2016
MAIL@FUSEARCHITECTURE.COM.AU
PHONE 02 8278 7156
ABN 51 612 048 643
NOMINATED ARCHITECT RACHID ANDARY NSW ARB 8627

CLIENT
CPS Planning on behalf of Landmark Element Pty Ltd
Level 3, 397 Riley Street, Surry Hills NSW 2010
Broadway NSW 2007

0 2 5 10m

SITE ADDRESS
18-24 Princes Hwy Kogarah NSW 2217 Australia

JOB NO 2614
CHECKED RA/AC
DRAWN AS/JA/JL
DATE APR 2026
SCALE 1:250 @ B1 A3@42%
PROJECT STATUS PRELIMINARY
DRAWING TITLE SITE ANALYSIS
SHEET NO SSDA 004
REVISION